
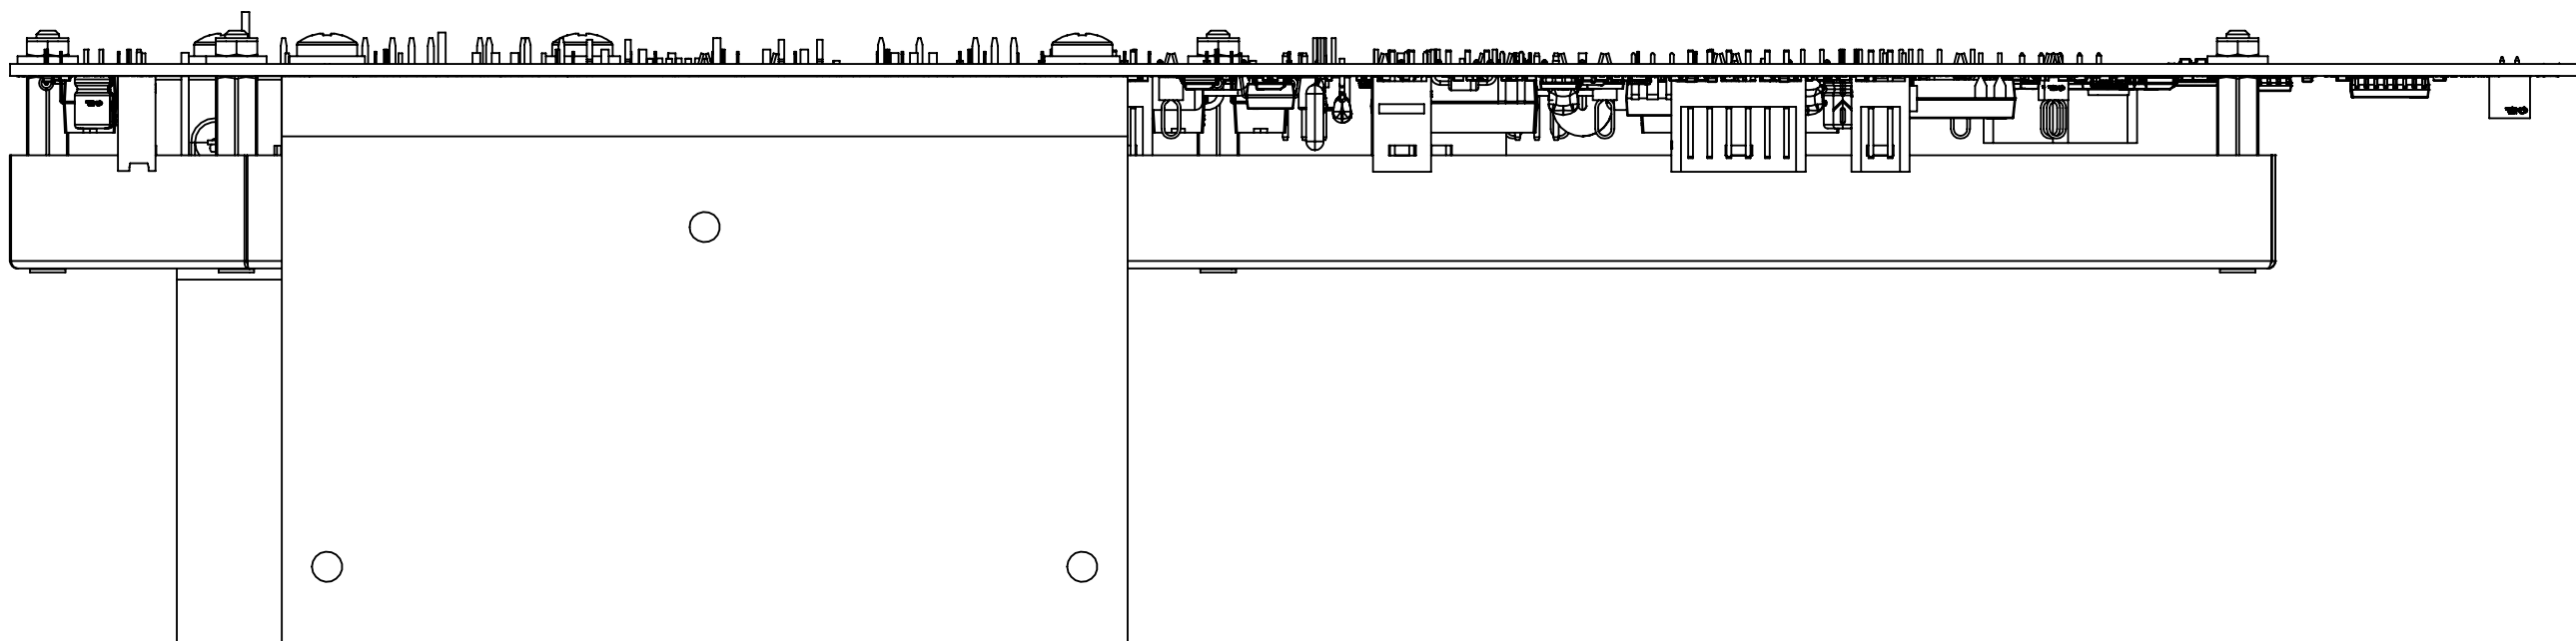
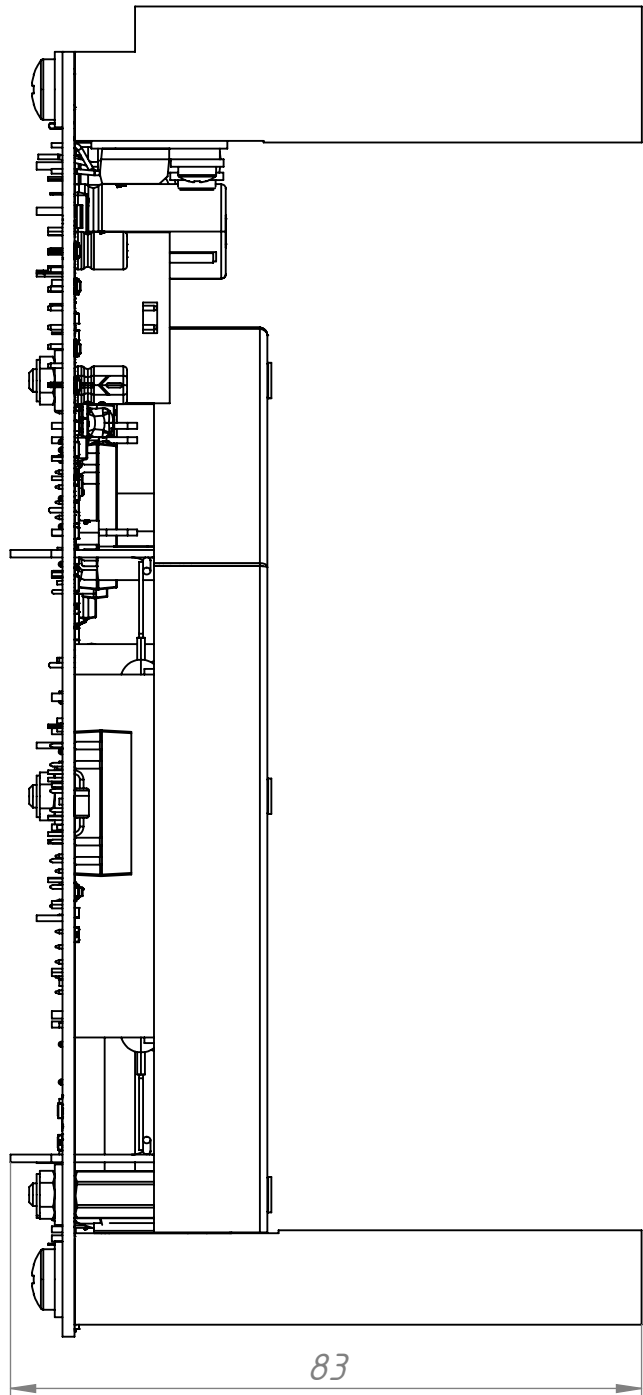


Инв. № подл.	Подп. и дата	Взам. инв. №	Инв. № дудл.	Подп. и дата	Справ. №	Перв. примен.
--------------	--------------	--------------	--------------	--------------	----------	---------------

УШЯИ.411618.0293 СБ

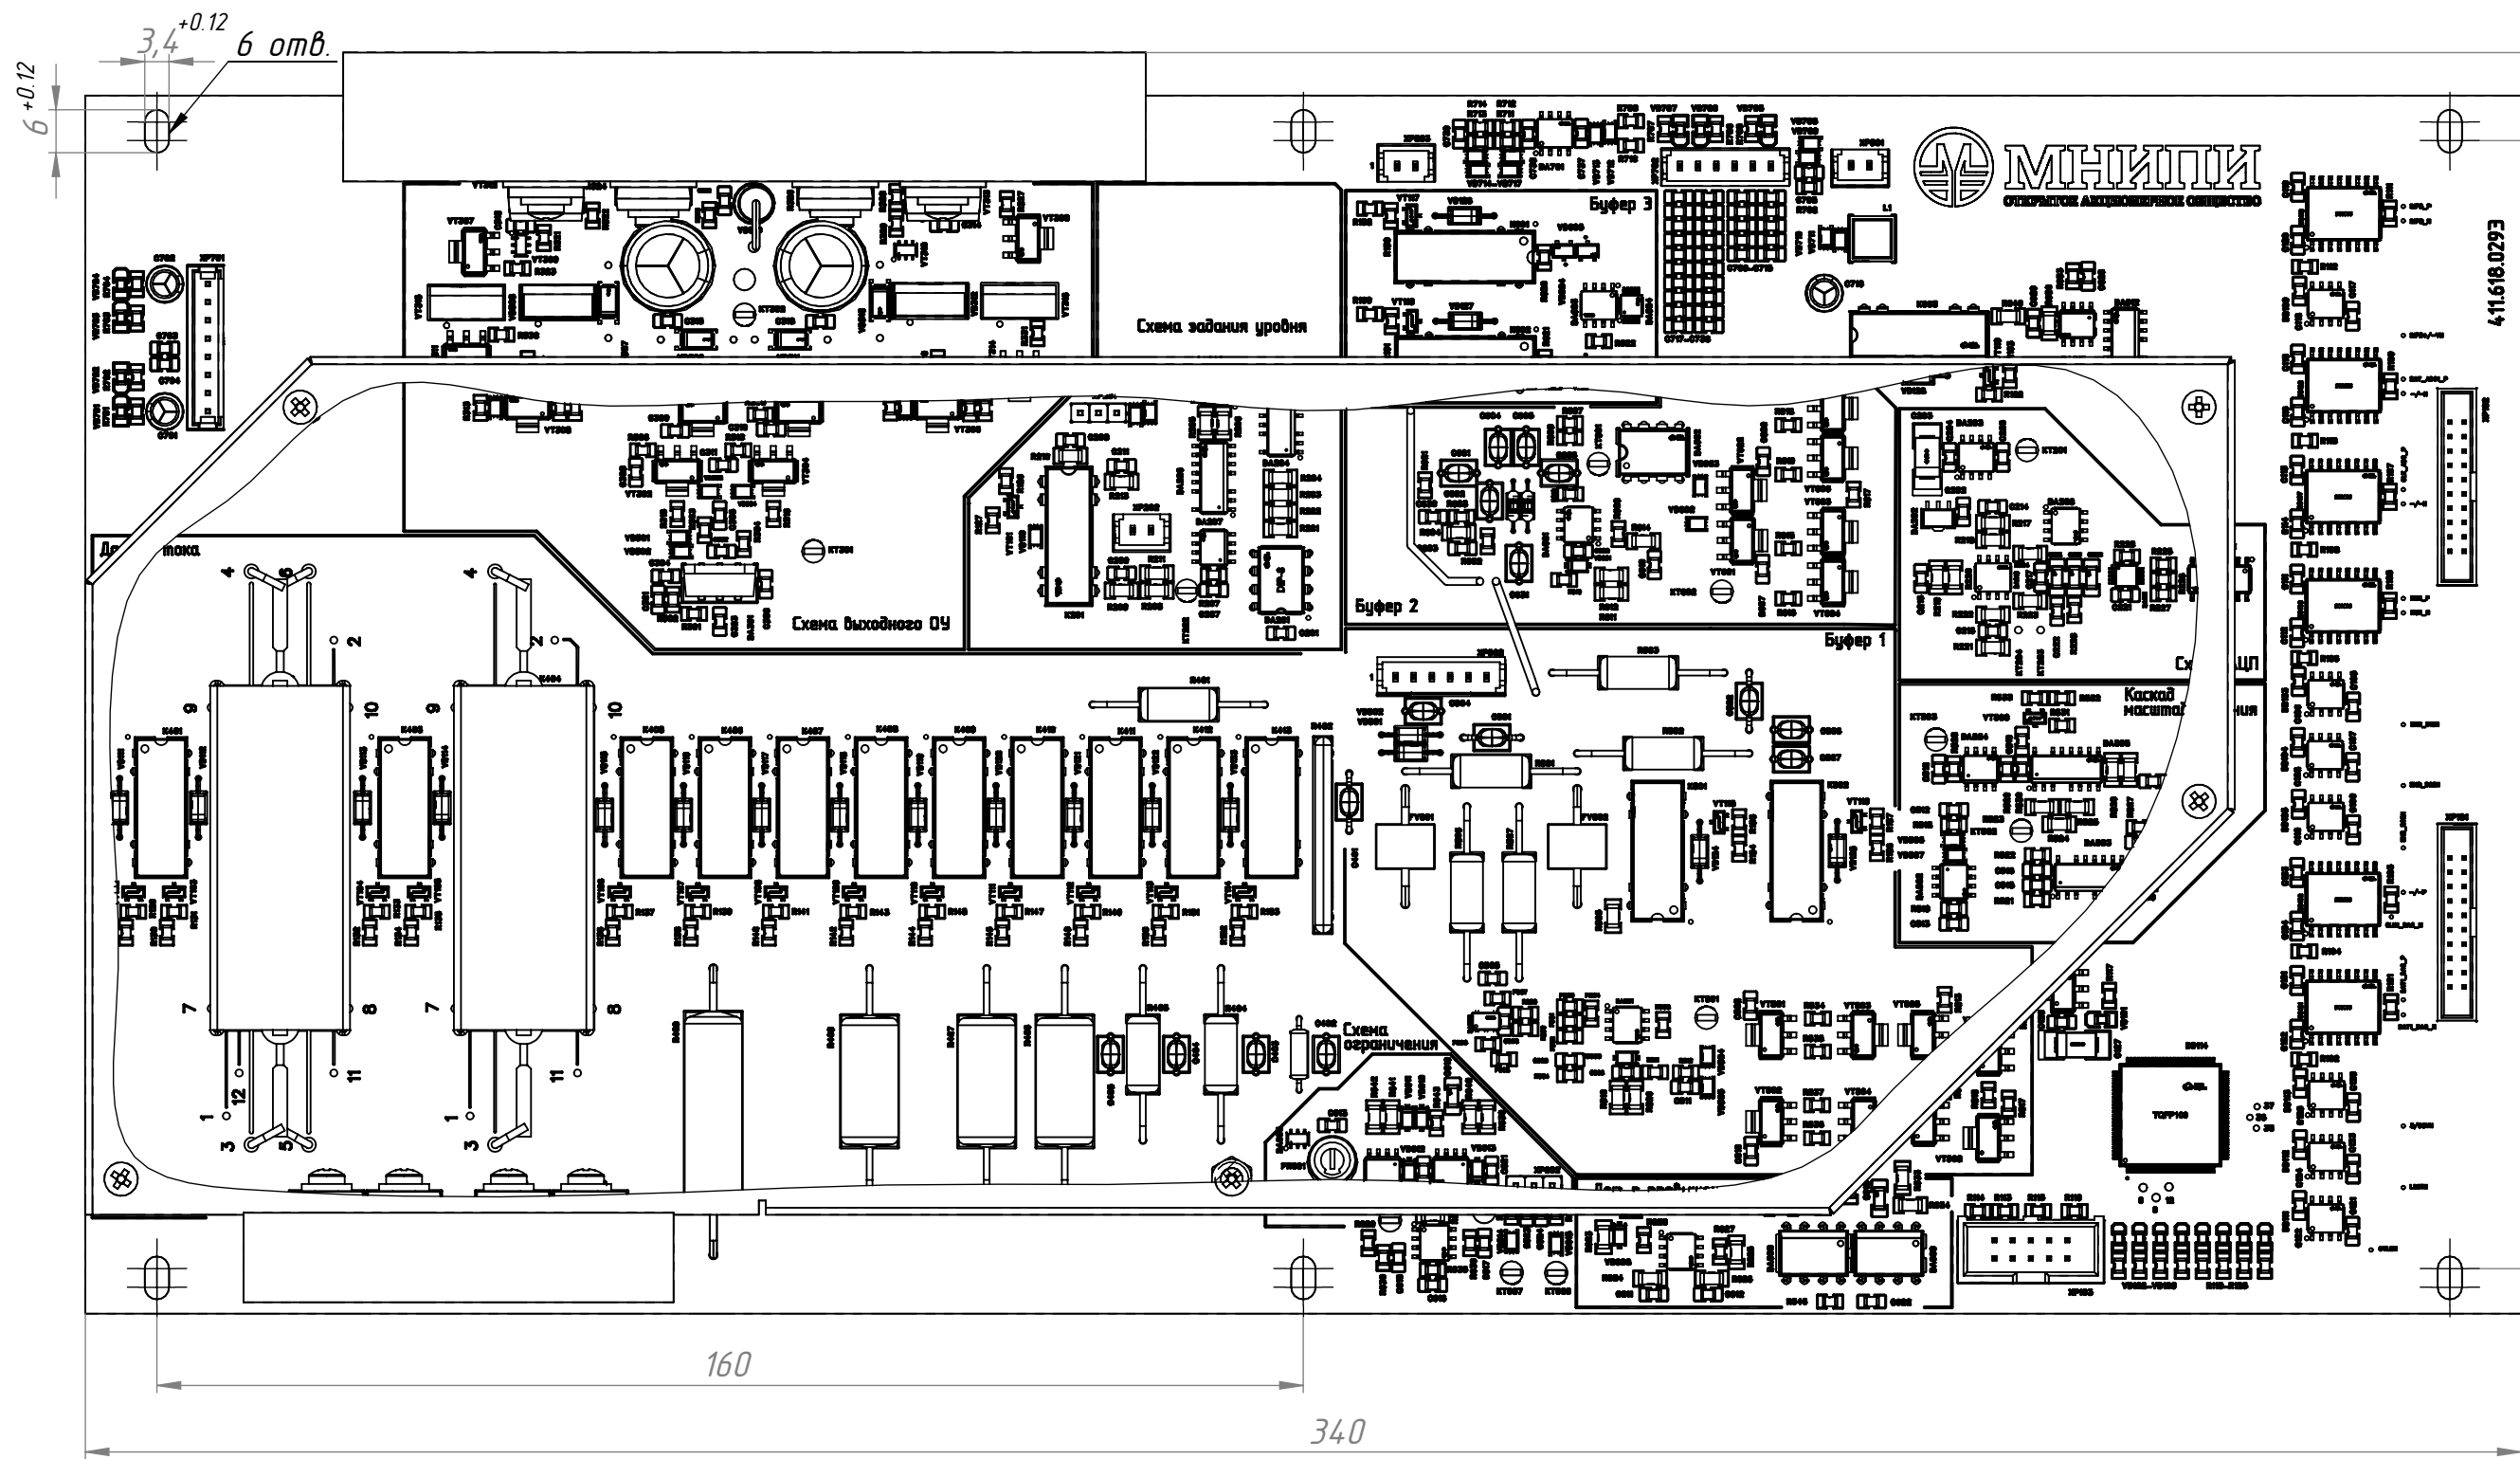

- 1 * Размеры для справок.
2 Монтаж элементов К402, К404, ДА301 выполнить согласно чертежу лист 2.
3 Монтаж элементов не указанных на листе 2 производить по ОСТ4.010.030-81.
4 ПСС-61 ГОСТ 21931-76.
5 Монтаж перемычек выполнить проволокой поз.51.
6 Технические требования к разделке и креплению жил проводов по ГОСТ 23587-96.
Размер ступени от 3 до 5 мм.
7 Технические требования к монтажу ЭРЗ по ГОСТ 23592-96.
8 Меры защиты ИМС и ППП от статического электричества по Тз.25000.00003.
9 Остальные технические требования по СТБ 1022-96.

					УШЯИ.411618.0293 СБ				
					Источник-измеритель Канал базы Чертёж сборочный	Лит.		Масса	Масштаб
Изм.	Лист	№ докум.	Подп.	Дата					1:1
Разраб.		Ефименко							
Пров.		Нестеров							
Т. контр.		Андрянчик				Лист 1	Листов 2		
Н. контр.		Толстый				ОАО "МНИПИ"			
Утв.		Володкевич							